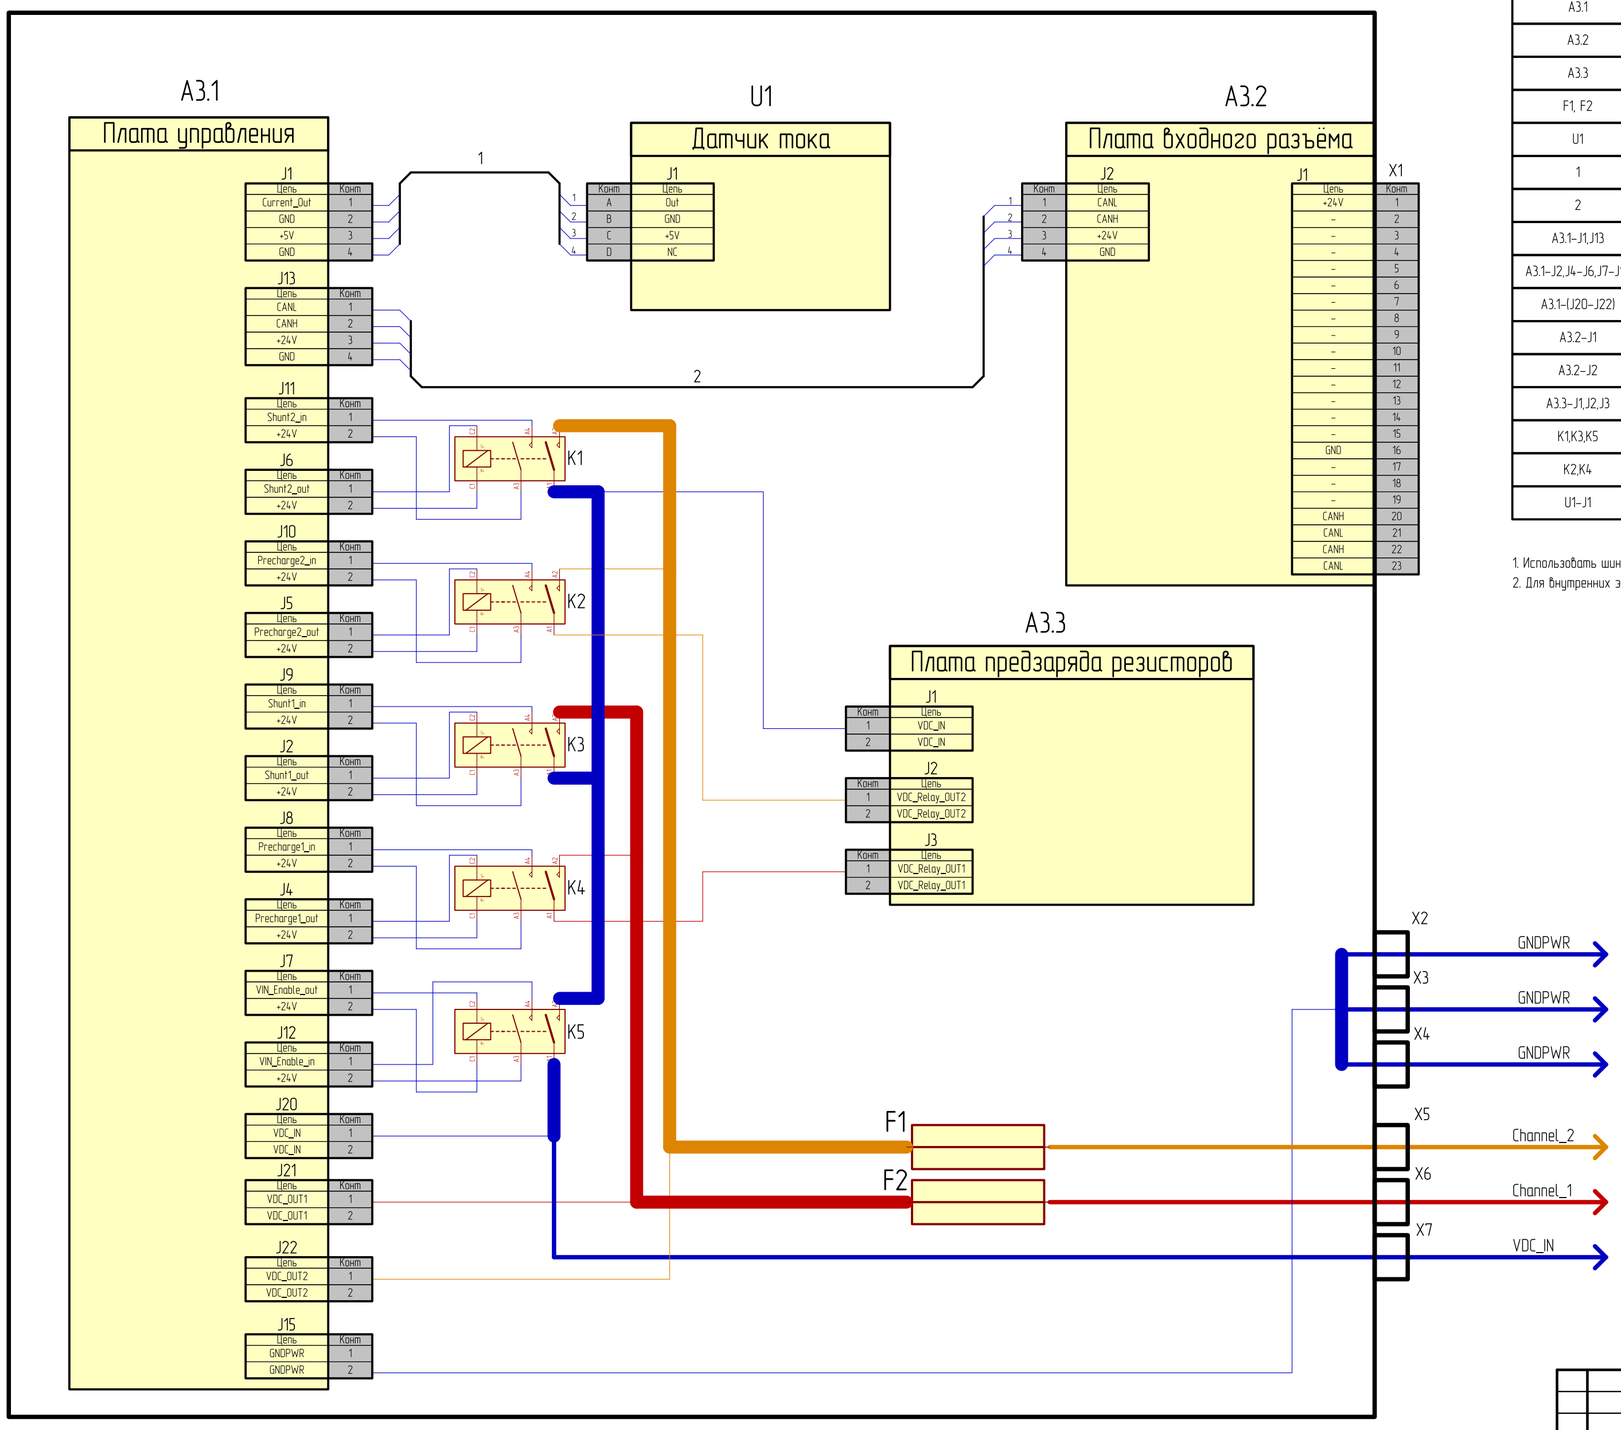

Поз. обозначение	Наименование	Кол.	Примечание
А3	Блок распределения питания силовой	1	
А3.1	Плата управления	1	
А3.2	Плата входного разъёма	1	
А3.3	Плата предзаряда резисторов	1	
F1, F2	Предохранитель	2	
U1	Датчик тока	1	
1	Жгут НВЦТ.0001.0400.500	1	Провод ММП (АМП)-Н50-0.35
2	Жгут НВЦТ.0001.0400.600	1	Провод ММП (АМП)-Н50-0.35
А3.1-J1,J13	Розетка на кабель MF-2x2F	2	Контакт KLS1-4.20-FT
А3.1-J2,J4-J6,J7-J12	Розетка на кабель KLS1-4.20-2x01-MH	11	Контакт KLS1-4.20-FT
А3.1-(J20-J22)	Розетка на кабель KLS1-4.20-2x01-MH	3	Контакт KLS1-4.20-FT
А3.2-J1	Розетка на кабель 770680-1	1	Контакт 770520-1
А3.2-J2	Розетка на кабель MF-2x2F	1	Контакт KLS1-4.20-FT
А3.3-J1,J2,J3	Розетка на кабель KLS1-4.20-2x01-MH	3	Контакт KLS1-4.20-FT
K1,K3,K5	Контактор EV200	3	
K2,K4	Контактор SVC50	2	
U1-J1	Розетка на кабель 1473672-1	1	Контакт 1123343-1

1. Использовать шины сечением 3х15мм.
2. Для внутренних электрических соединений использовать провод ММП (АМП)-Н50-0.35.

Изм.	Лист	N°докум.	Подп.	Дата	НВЦТ.0001.0400.100_v1. Э4
Разраб.		Филатов А.С.			Блок распределения питания силовой Схема электрическая соединений
Пров.		Сизякин А.В.			Лит. / Масса / Масштаб
Т.контр.					Лист 1 / Листов 1
Н.контр.		Зубков Д.Н.			ООО "Электротранспортные технологии"
Утв.		Коваленко В.А.			

Перв. примен. НВЦТ.0001.0400.100
Справ. N°
Подп. и дата
Инв.N°дубл.
Взам.инв.N°
Подп. и дата
Инв.N°подл.

Копировал

Формат А2