

A3.1


Плата управления

U1

Датчик тока

A3.2

Плата входного разъёма

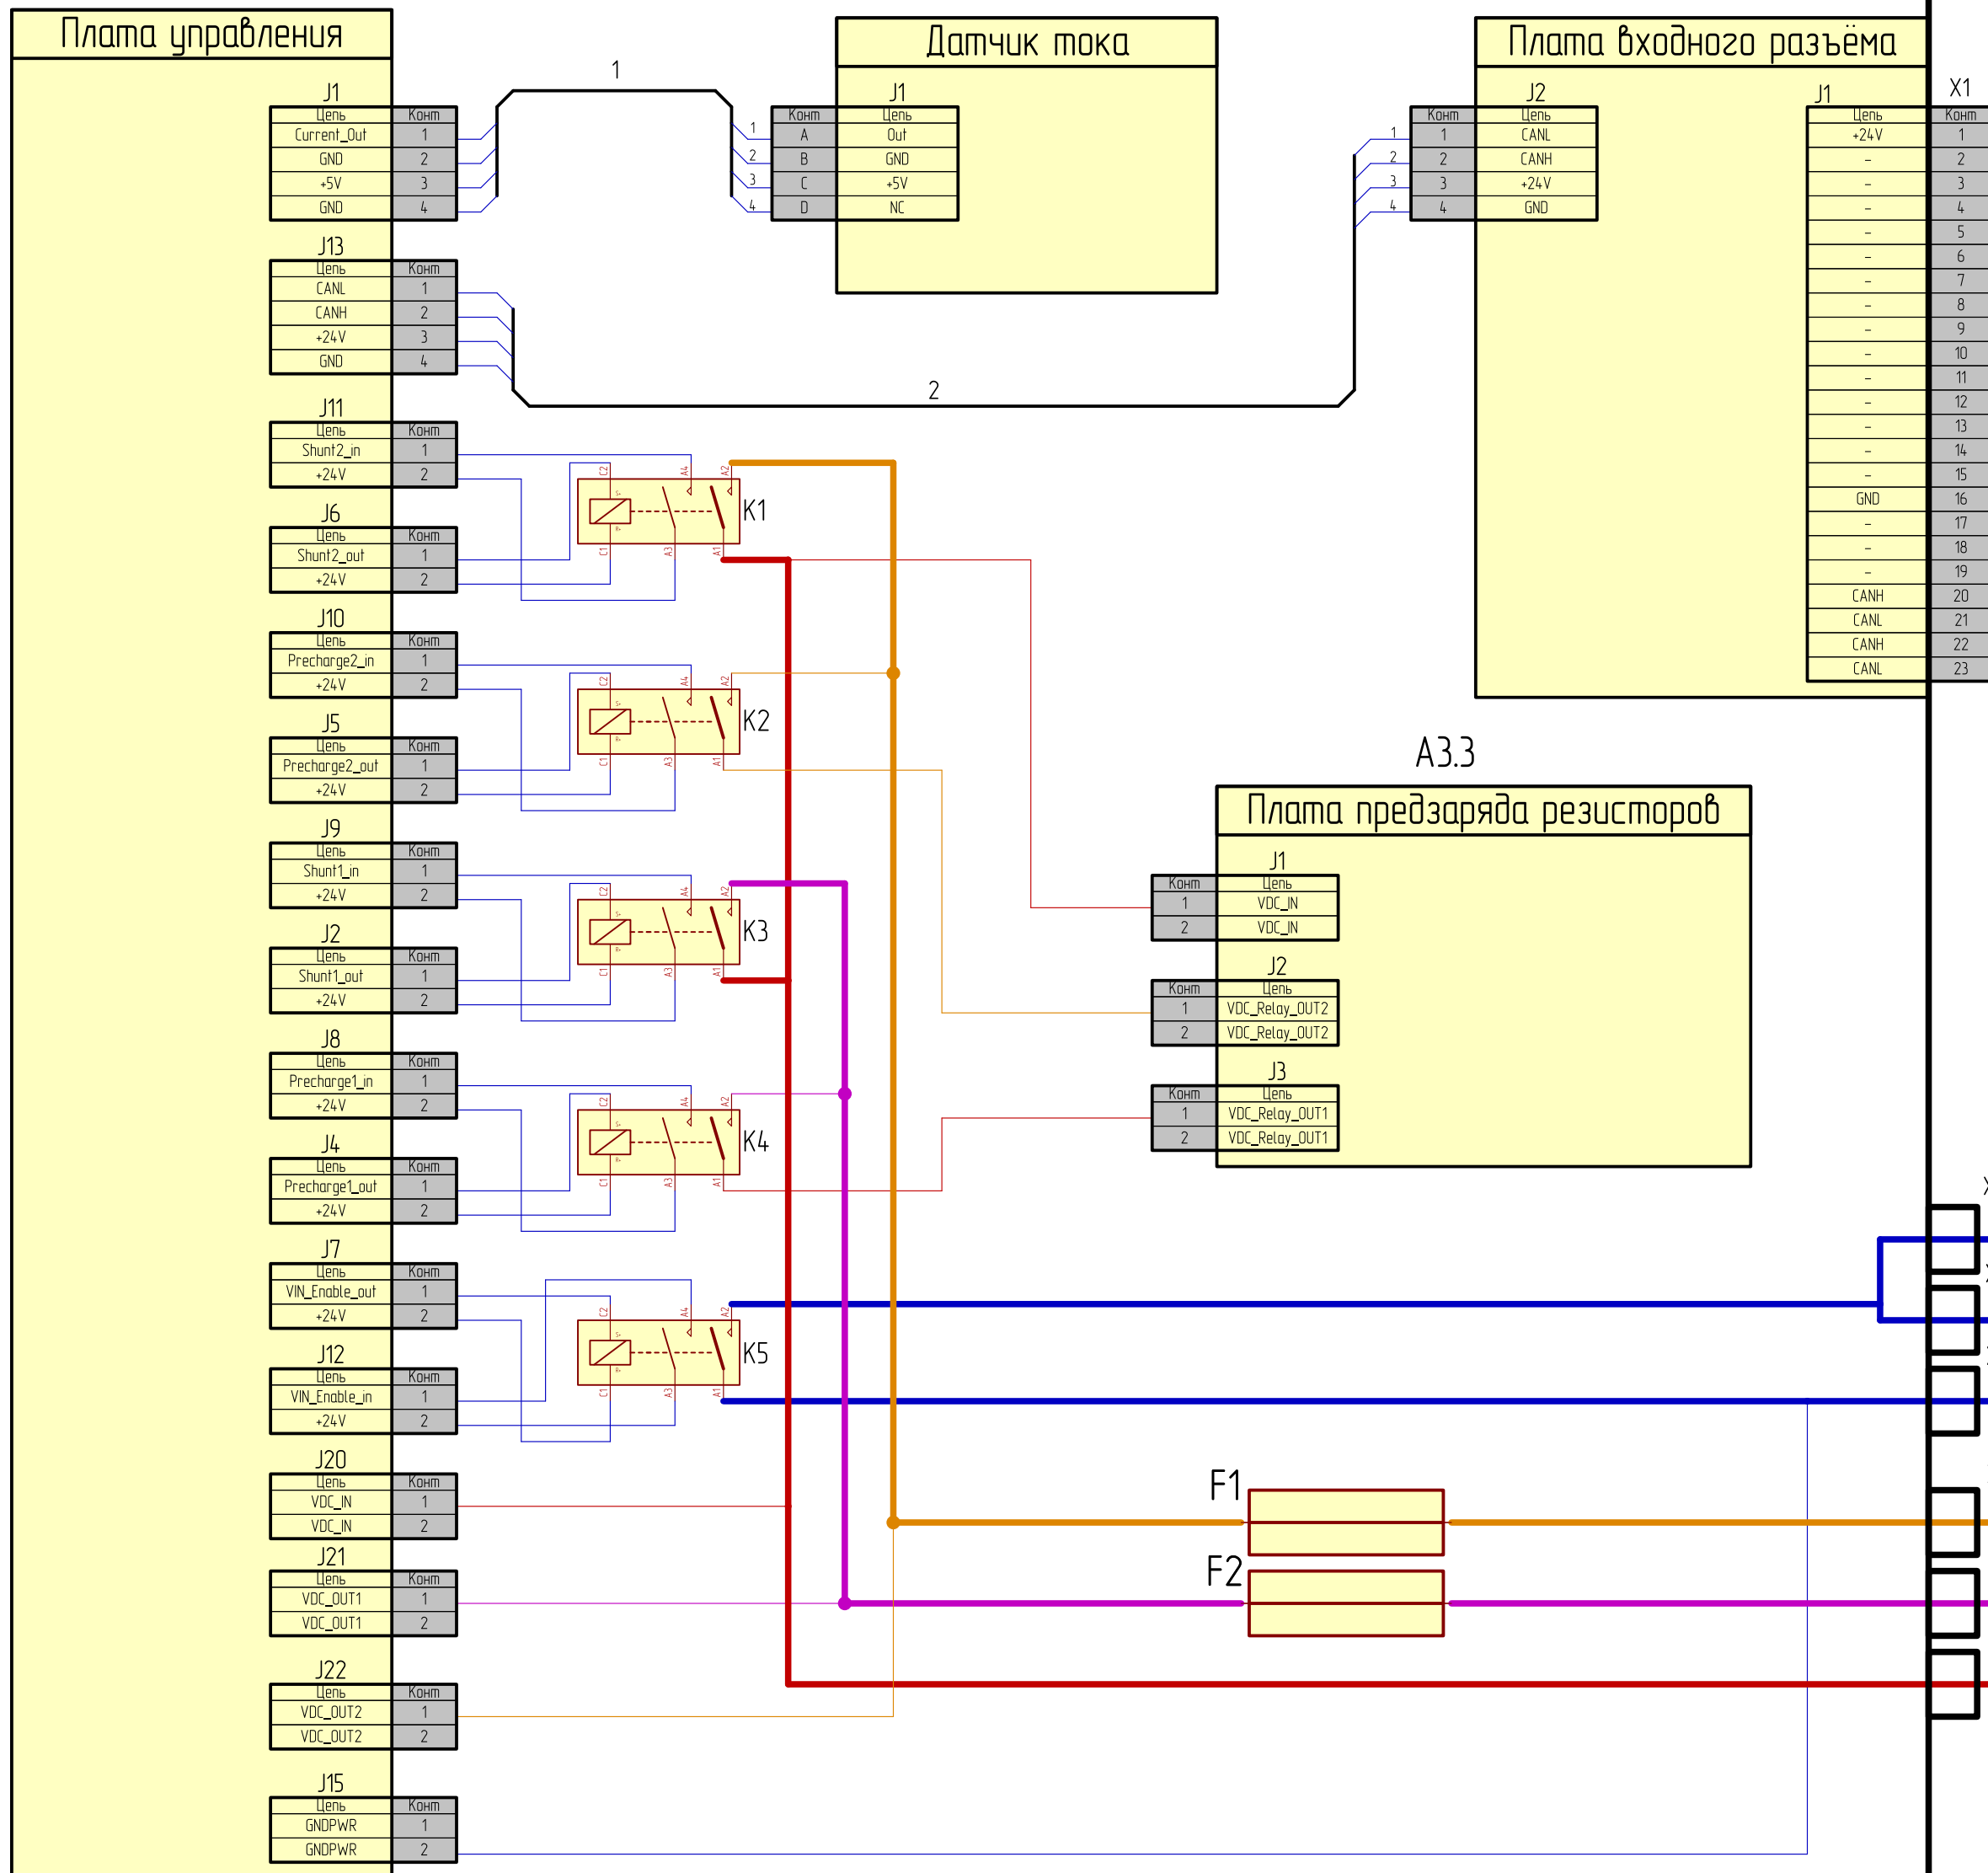

1. Использовать шины сечением 3х15мм.
2. Для внутренних электрических соединений использовать провод ММП (АМР)–Н50–0.35.

Поз. обозначение	Наименование	Кол.	Примечание
A3	Блок распределения питания силовой	1	
A3.1	Плата управления	1	
A3.2	Плата входного разъёма	1	
A3.3	Плата предзаряда резисторов	1	
F1, F2	Предохранитель	2	
U1	Датчик тока	1	
1	Жгут НВЦТ.00010400.500	1	Провод ММП (АМР)-H50-0.35
2	Жгут НВЦТ.00010400.600	1	Провод ММП (АМР)-H50-0.35
A3.1-J1,J3	Разетка на кабель MF-2x2F	2	Контакт KLS1-4.20-FT
A3.1-J2,J4-J6,J7-J12	Разетка на кабель KLS1-4.20-2x01-MH	11	Контакт KLS1-4.20-FT
A3.1-(J20-J22)	Разетка на кабель KLS1-4.20-2x01-MH	3	Контакт KLS1-4.20-FT
A3.2-J1	Разетка на кабель 770680-1	1	Контакт 770520-1
A3.2-J2	Разетка на кабель MF-2x2F	1	Контакт KLS1-4.20-FT
A3.3-J1,J2,J3	Разетка на кабель KLS1-4.20-2x01-MH	3	Контакт KLS1-4.20-FT
K1,K3,K5	Контактор EV200	3	
K2,K4	Контактор SVC50	2	
U1-J1	Разетка на кабель 1473672-1	1	Контакт 1123343-1

						НВЦТ.0001.0400.100_v1 Э4						
1	Зам.	НВЦТ.0001006				Блок распределения питания силовой Схема электрическая соединений			Лист		Масса	Масштаб
Изм	Лист	№докум.	Подп.	Дата								
Разработ.	Филатов А.С.											
Проб.	Сизякин А.В.											
Т.контр.					Лист				1	Листов	1	
Н.контр.	Зубов Д.Н.					000 "Электротранспортные технологии"						
Утв.	Коваленко В.А.											