


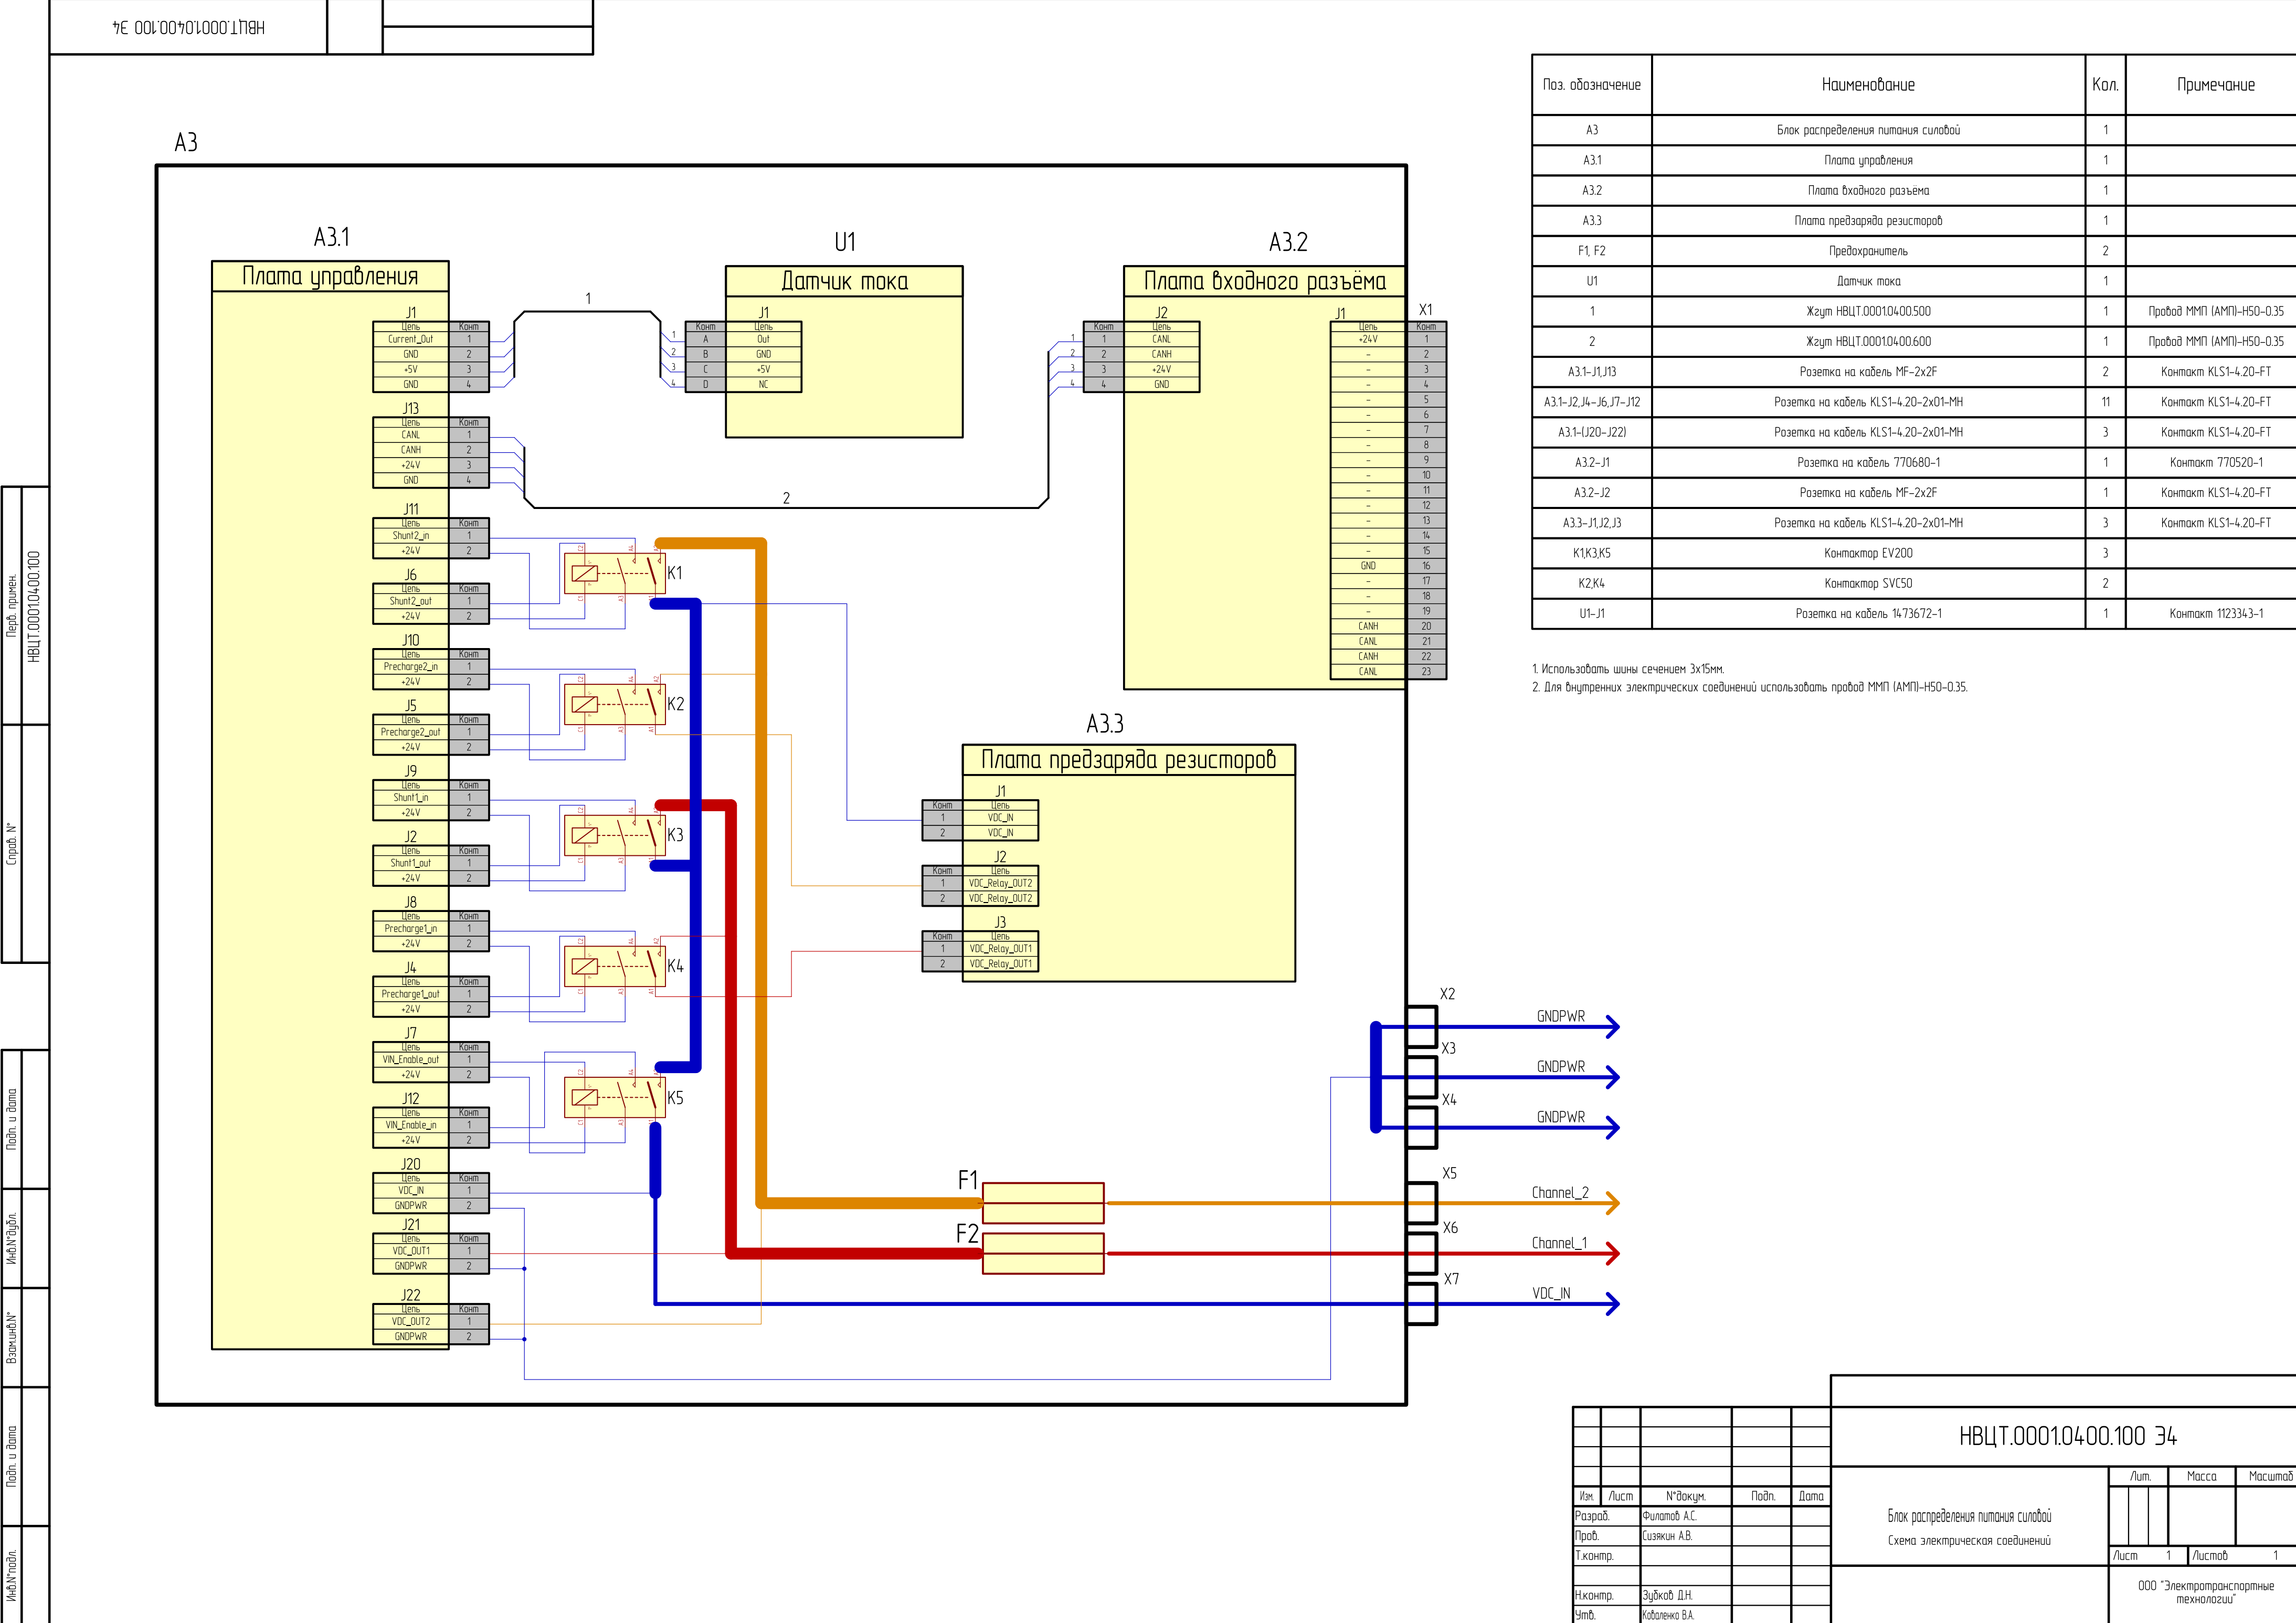

J2

Цель

Shunt1_out

1

Конп

2

+24V

J8

Цель

Precharge1_in

1

Конп

2

+24V

J4

Цель

Precharge1_out

1

Конп

2

+24V

J7

Цель

VIN_Enable_out

1

Конп

2

+24V

J12

Цель

VIN_Enable_in

1

Конп

2

+24V

J20

Цель

VDC_IN

1

Конп

2

GNDPWR

J21

Цель

VDC_OUT1

1

Конп

2

GNDPWR

J22

Цель

VDC_OUT2

1

Конп

2

GNDPWR

1

2

3

4

J1

Цель

Out

1

Конп

2

GND

3

+5V

4

NC

2

A3.2

Плата входного разъёма

J2

Конп

1

Цель

CANL

2

CANH

3

+24V

4

GND

J1

Цель

+24V

1

Конп

2

-

3

-

4

-

5

-

6

-

7

-

8

-

9

-

10

-

11

-

12

-

13

-

14

-

15

-

16

GND

17

-

18

-

19

-

20

CANH

21

CANL

22

CANH

23

CANL

X1

Конп

1

Цель

+24V

2

-

3

-

4

-

5

-

6

-

7

-

8

-

9

-

10

-

11

-

12

-

13

-

14

-

15

-

16

GND

17

-

18

-

19

-

20

CANH

21

CANL

22

CANH

23

CANL

A3.3

Плата предзаряда резисторов

J1

Конп

1

Цель

VDC_IN

2

VDC_IN

J2

Конп

1

Цель

VDC_Relay_OUT2

2

VDC_Relay_OUT2

J3

Конп

1

Цель

VDC_Relay_OUT1

2

VDC_Relay_OUT1

F1

F2

X2

X3

X4

X5

X6

X7

GNDPWR

GNDPWR

GNDPWR

Channel_2

Channel_1

VDC_IN

Перв. примен.

НВЦТ.0001.04.00.100

Справ. №

Подп. и дата

Инф.№докл.

Вариант.№

Подп. и дата

Инф.№докл.

Поз. обозначение	Наименование	Кол.	Примечание
A3	Блок распределения питания силовой	1	
A3.1	Плата управления	1	
A3.2	Плата входного разъёма	1	
A3.3	Плата предзаряда резисторов	1	
F1, F2	Предохранитель	2	
U1	Датчик тока	1	
1	Жгут НВЦТ.0001.04.00.500	1	Провод ММП (АМП)-H50-0.35
2	Жгут НВЦТ.0001.04.00.600	1	Провод ММП (АМП)-H50-0.35
A3.1-J1, J13	Разетка на кабель MF-2x2F	2	Контакт KLS1-4.20-FT
A3.1-J2, J4-J6, J7-J12	Разетка на кабель KLS1-4.20-2x01-MH	11	Контакт KLS1-4.20-FT
A3.1-(J20-J22)	Разетка на кабель KLS1-4.20-2x01-MH	3	Контакт KLS1-4.20-FT
A3.2-J1	Разетка на кабель 770680-1	1	Контакт 770520-1
A3.2-J2	Разетка на кабель MF-2x2F	1	Контакт KLS1-4.20-FT
A3.3-J1, J2, J3	Разетка на кабель KLS1-4.20-2x01-MH	3	Контакт KLS1-4.20-FT
K1, K3, K5	Контактор EV200	3	
K2, K4	Контактор SVC50	2	
U1-J1	Разетка на кабель 1473672-1	1	Контакт 1123343-1

1. Использовать шины сечением 3х15мм.

2. Для внутренних электрических соединений использовать провод ММП (АМП)-H50-0.35.

Иж

Лист

№докум.

Подп.

Дата

Разраб.

Филатов А.С.

Проб.

Сузякин А.В.

Т.контр.

Н.контр.

Зубков Д.Н.

Утв.

Кабаленко В.А.

НВЦТ.0001.04.00.100 34

Блок распределения питания силовой

Схема электрическая соединений

Лист

1

Листов

1

000 "Электротранспортные технологии"

Копировал

Формат А2